


3D MODEL

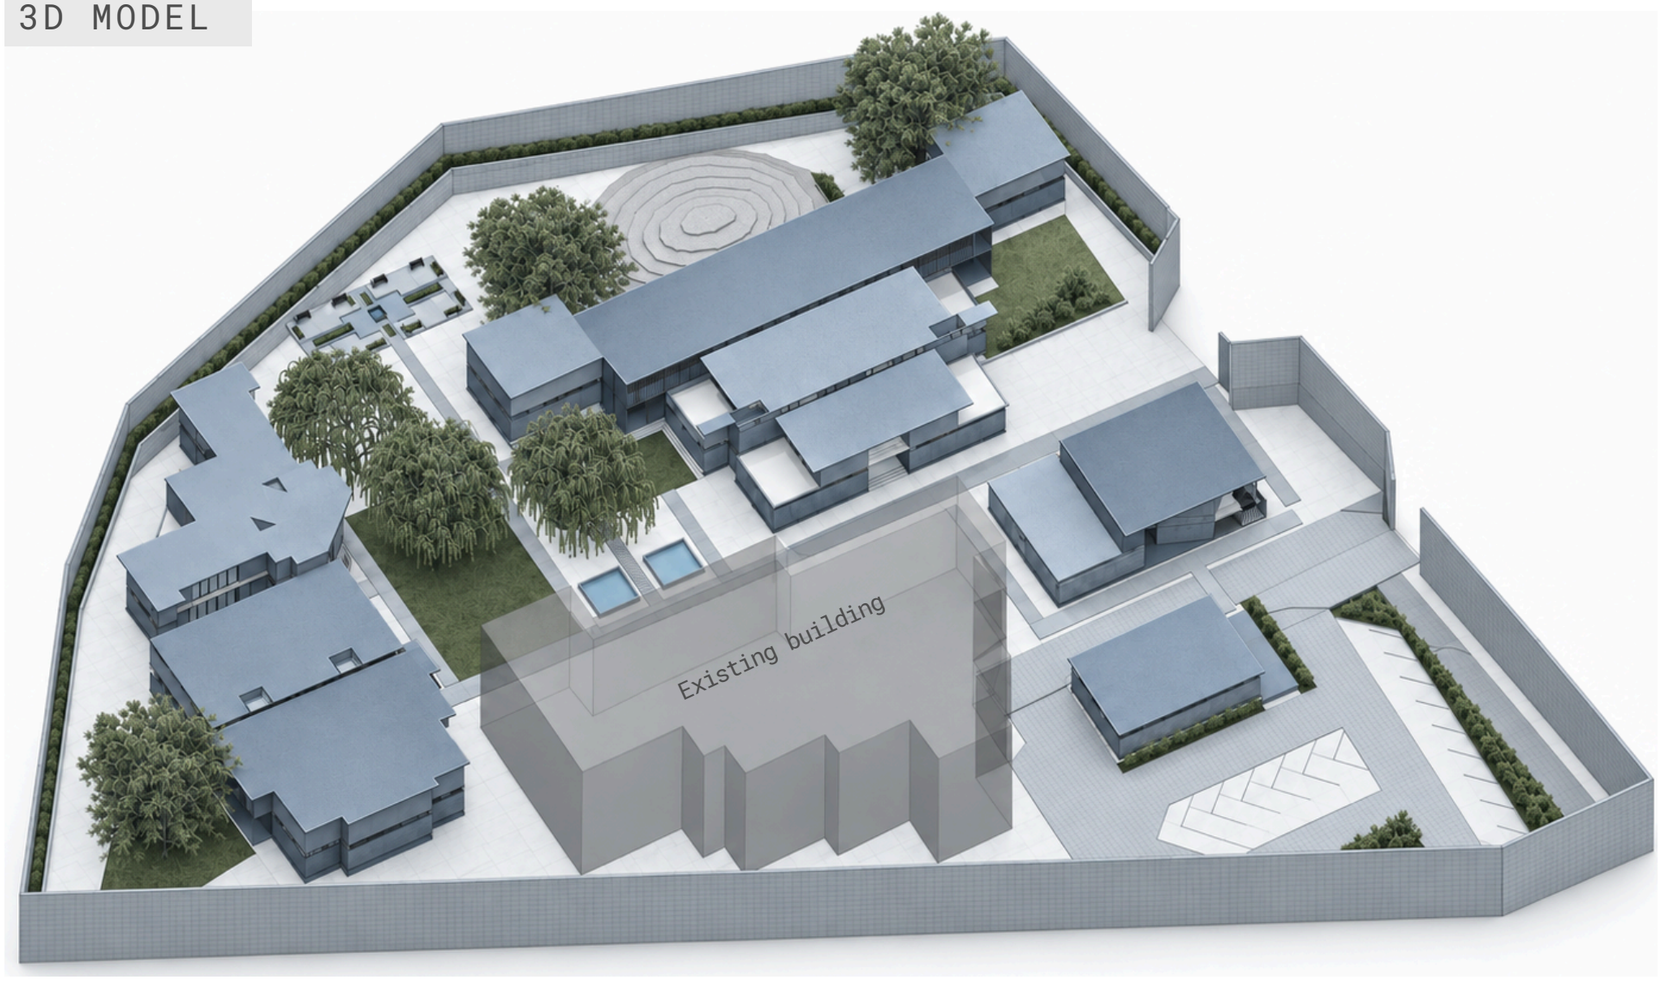


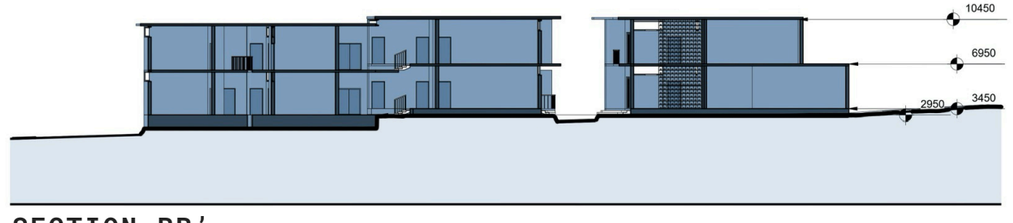


SECTION BB'

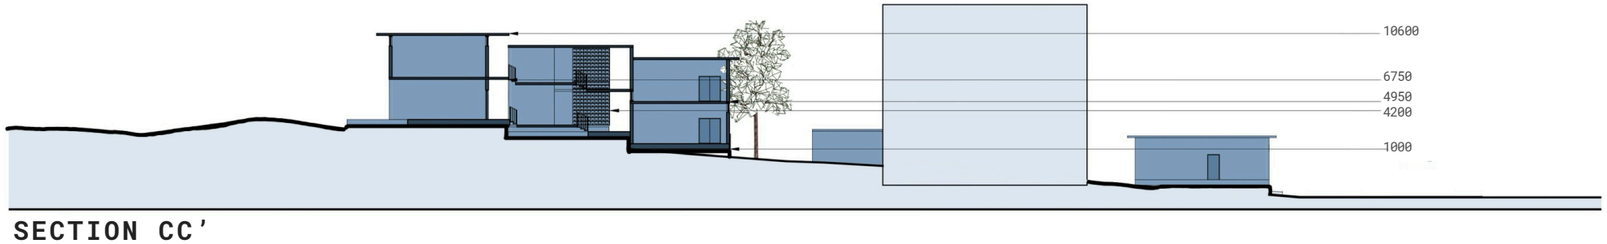

SECTION CC'

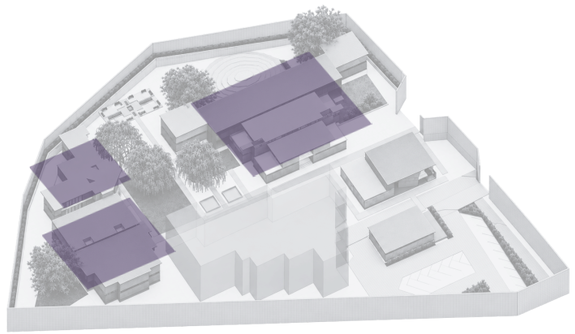

Varied spatial form → varied experience

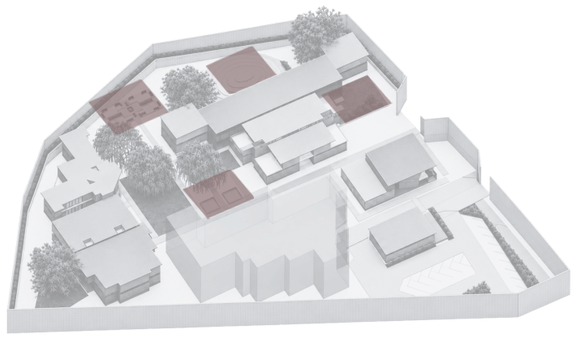

Distinct sensory landmarks



Visual Arts Block Lobby



Existing Boulder as Social Anchor